



Plantation
the grass is greener®

Notice of Plantation Gateway Advisory Board Meeting

City Hall, First Floor Conference Room
400 NW 73rd Ave
Plantation, Florida 33317

October 19, 2022 – 11:00 AM

1. CALL TO ORDER/ROLL CALL

2. APPROVAL OF MEETING MINUTES

[2022-08-17 Meeting Minutes](#)

3. GATEWAY FINANCIAL REPORT - September 2022 *presented by Glendon Hall*

4. DEVELOPMENT UPDATE *presented by Glendon Hall*

5. GATEWAY POLICING/CODE UPDATE *presented by Lt. Rudy Brown/Pete Saglio*

6. GATEWAY ENGINEERING UPDATE *presented by Samira Shalan*

7. NEW BUSINESS

- [HCA Development Update](#)

8. ADJOURNMENT

Next Meeting: Wednesday, December 21, 2022

Notice: *The City of Plantation will provide reasonable accommodations for disabled individuals requesting special assistance in order to attend or participate in this meeting; provided however, that a request for such assistance must be made to the Office of the City Clerk (954) 797-2237 at least five (5) calendar days prior to the meeting.*

Any member of the public who wishes to make comments via email prior to the meeting should send the email comments to the City Clerk's Office at abeggerow@plantation.org no later than 12:00 p.m. the day prior to the scheduled meeting. More than 1 elected official may be in attendance.



**PLANTATION GATEWAY ADVISORY BOARD CITY HALL, FIRST FLOOR
CONFERENCE ROOM 400 NW 73RD AVE
PLANTATION, FLORIDA 33317
WEDNESDAY, OCTOBER 19, 2022**

Present: Dwight Brady, Dean Bromante, Kenneth Anson, Kevin Bingham, Mike Hooley Jr.,
Natasha DeWet

Absent: LeRoy L Larson

Also Present: Carole Morris, Samira Shalon, Dan Holmes, Michael Alpert, Glen Hall, Jason
Nunemaker, Mayor Stoner, Councilmember Horland, Lt. Rudy Brown, Officer Chad Fowler,
Officer Riveria, Kristin Hinsley, Scott Raysey, Louis Reinstein

1. CALL TO ORDER/ROLL CALL

The members went about the room and introduced themselves.

2. APPROVAL OF MEETING MINUTES

Motion to approve as submitted by Mike Hooley Jr., seconded by Dean Bromante.

Motion Passed by Consensus

6 - 0

2022-08-17 Meeting Minutes

[2022-08-17 Minutes.pdf](#)

3. GATEWAY FINANCIAL REPORT - September 2022 presented by Glendon Hall

Planning and Zoning staff Glendon Hall reported to the Board the Financial Report as of
August for the fiscal year, attached to the minutes, current year additions/deletions,

revenues, and expenditures. He stated the expenditures are normal and revenues have right where we typically should be as of August 2022 in terms of revenue. The assets and liability are equaling out.

Gateway Financials Report - August 22

4. DEVELOPMENT UPDATE *presented by Glendon Hall*

Mr. Hall gave an update on the current development project that has started within the Gateway District. He reporting CareMax Daycare is the only new development at this moment all other projects are still ongoing.

Development Report - October 2022

[Development Report 10-22.pdf](#)

5. GATEWAY POLICING/CODE UPDATE *presented by Lt. Rudy Brown/Pete Saglio*

Lt. Rudy Brown of the Plantation Police Department discussed the crime statics and policing within the Gateway corridor, he stated the overtime position fulfillment rate is at 99%. He reported to the Board regarding the pity thief that is occurring at Walgreens, the Plantation Inn arrests that are being made for burglaries of empty rooms, and the weapons that were seized during the arrests.

Mr. Hooley recognized Officer Riviera for his exceptional work and commitment to the Gateway Corridor.

6. GATEWAY ENGINEERING UPDATE *presented by Samira Shalan*

Engineering Director Samira Shalan address the Board regarding the Welcome to Plantation Entry Signage project on Sunrise Boulevard, east of NW 43rd Avenue. She shared the contract plans of the project and announced the new Google Earth Map that the Engineering Department has launched. She reported that the City landscape project is 90% completed, gave timelines for the phases that will be starting, and stated that the Public Works Department will maintain the lightning.

7. NEW BUSINESS

[HCA Development Update](#)

HCA Westside Hospital Vice President of Development Kristin Hinsley presented to the Board the three-phase approach that the hospital has proposed to take in the transition from the old Plantation Hospital into a freestanding Emergency Room. She provided details

of the proposal submission, the location of the new building, the parking lot layout, the contractors' quote that was obtained, the third-party evaluation, and the services that will be provided.

A discussion ensued among the Board Members and the HCA representatives.

[City of Plantation- Gateway October 2022 Meeting- HCA Presentation.pdf](#)

8. ADJOURNMENT

The meeting adjourned at 11:58 p.m.

Next Meeting: Wednesday, December 21, 2022



The Next Generation of Plantation General Campus


October 2022

CONFIDENTIAL – Contains proprietary information.
Not intended for external distribution.



Recommending to build a new stand-alone FSER, and evaluate the remaining 8.6 acres for redevelopment

Plantation Campus with Proposed FSER

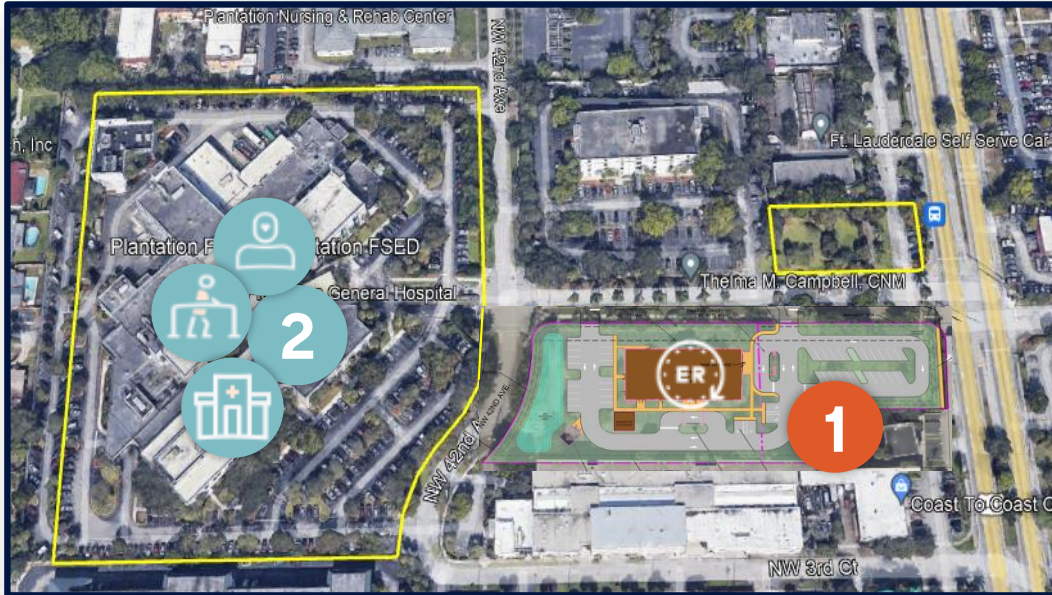

Market Dynamics

(5) Yr. Population Growth | Broward Mkt: (+4.5%) | PGH PSA: (+5.4%)

Advisory Board Projections

5 Yr. Trend (2026)

10 Yr. Trend (2031)

IP

OP

IP

OP

IP and OP Scenario Planner

Overall
-2.2%

Overall
+2.9%

Overall
-0.9%

Overall
+8.4%

Service Line Opportunity

IP
Rehab
+9.6%

OP
Psych
+12.5%

IP
Rehab
+18%

OP
Psych
+32%

Proposed Recommendations

(1)
Stand-alone
FSER

(2)
Building
Demolition

Progress

Submitted for
Approval

Engaged (3) Contractors
Quotes obtained



Opportunity Analysis



Medical Office Building



Behavioral Health



Inpatient Rehab/SNF

Service Line Evaluations

CONFIDENTIAL – Contains proprietary information.
Not intended for external distribution.

MAYOR
LYNN STONER

CITY COUNCIL
Erik Anderson, President
Jennifer Andreu, President Pro Tem
Timothy J. Fadgen
Denise Horland
Nick Sortal

CITY OF PLANTATION

ENGINEERING DEPARTMENT

CONTRACT PLANS

Welcome to Plantation Entry Sign


City Project No. CP22-06

INDEX OF DRAWINGS

<u>SHEET NO.</u>	<u>SHEET DESCRIPTION</u>
C-0	Cover Page
C-01	Project Location and Layout
C-02	Elevations
C-03	General Construction Notes
S-01	Sections
S-02	Details and Structural Notes



VICINITY MAP
NOT TO SCALE

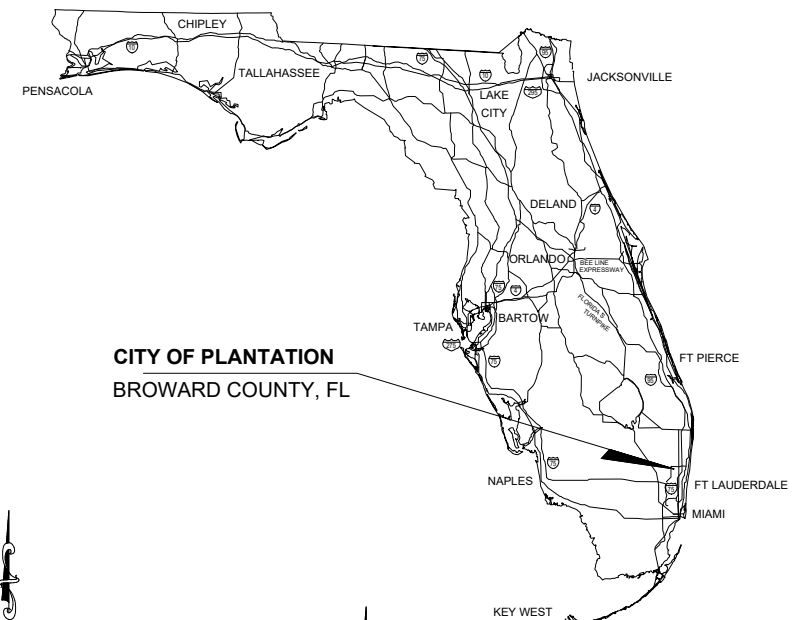

CITY OF PLANTATION
BROWARD COUNTY, FL


LOCATION MAP
NOT TO SCALE

PROJECT SCOPE:

Furnish and installation of (1) "Chicago Brick" entry sign. All work shall conform to the design requirements of these plans and contract documents.

PLANS PREPARED BY:

CITY OF PLANTATION
ENGINEERING DEPARTMENT
400 NW 73 AVENUE
PLANTATION, FL 33317

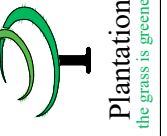

CITY OF PLANTATION

ENGINEERING DEPT.

401 NW 70TH TERRACE, PLANTATION, FL 33311

TEL. (954)797-2282 FAX (954) 797-2761

AMIRA SHALAN P.E.

CITY ENGINEER

DATE

No.	DATE	BY	COMMENT

Welcome to Plantation Entry Sign
Project Location and Layout

DRAWING

DATE	
N.T.S.	
SIGNED	DATE
DRAWN BY C. Riaño	DATE
CHECKED BY	DATE
DRAWING NO. C-01	
PROJECT NO.	
CP22-06	
SHEET NO.	



PROJECT LOCATION

SCALE: 1" = 40'-0"

LEGEND:

-  PROPOSED GROUND MOUNTED ENTRY SIGN
SEE C2 FOR DETAILS
-  TREE EVERY 40'. LANDSCAPING TO BE DESIGNED
BY OTHER. REFER TO LANDSCAPE PLAN.
-  TRAFFIC FLOW
-  FDOT RIGHT OF WAY


**CALL 48 HOURS
BEFORE YOU DIG**

**IT'S THE LAW!
DIAL 811**


**Know what's below.
Call before you dig.**

SUNSHINE STATE ONE CALL OF FLORIDA, INC.



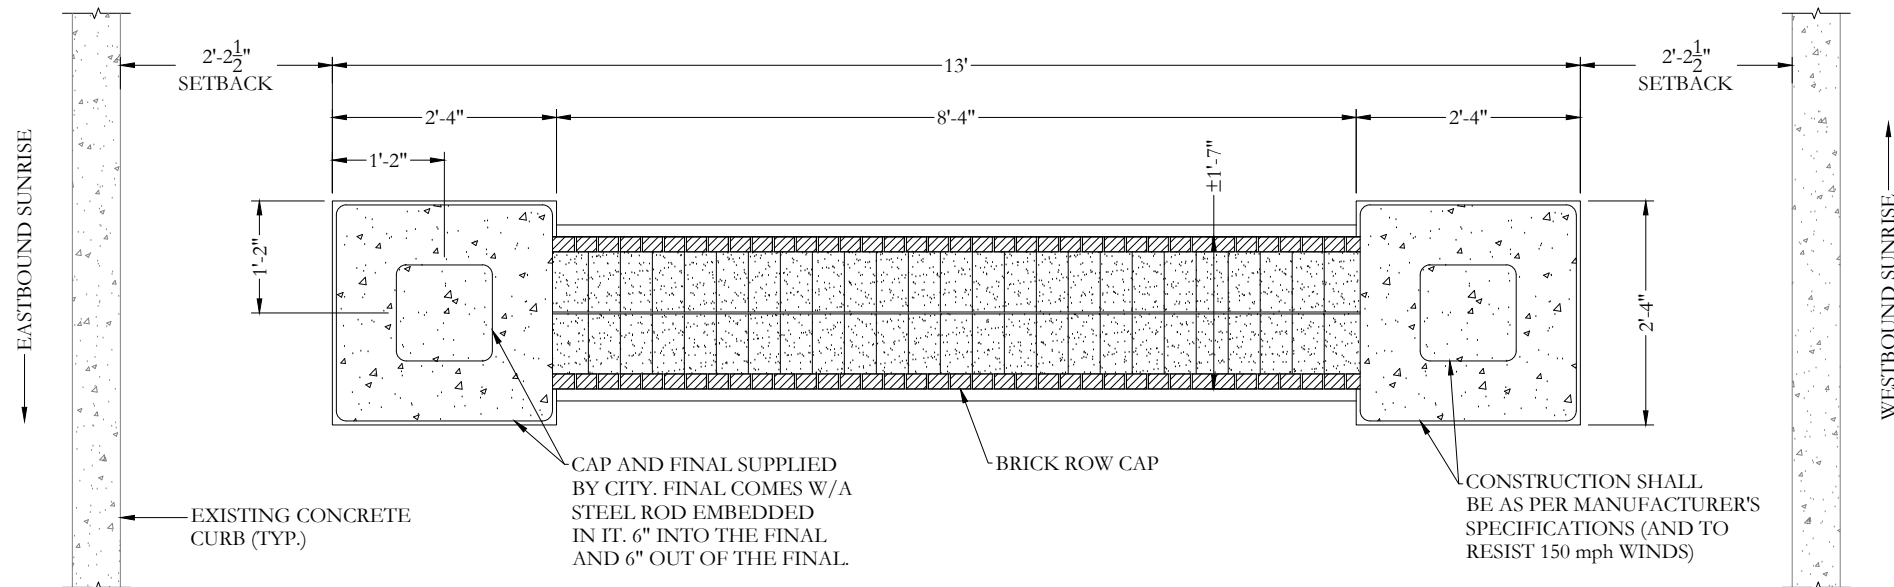

PROPOSED ENTRY SIGN TOP VIEW

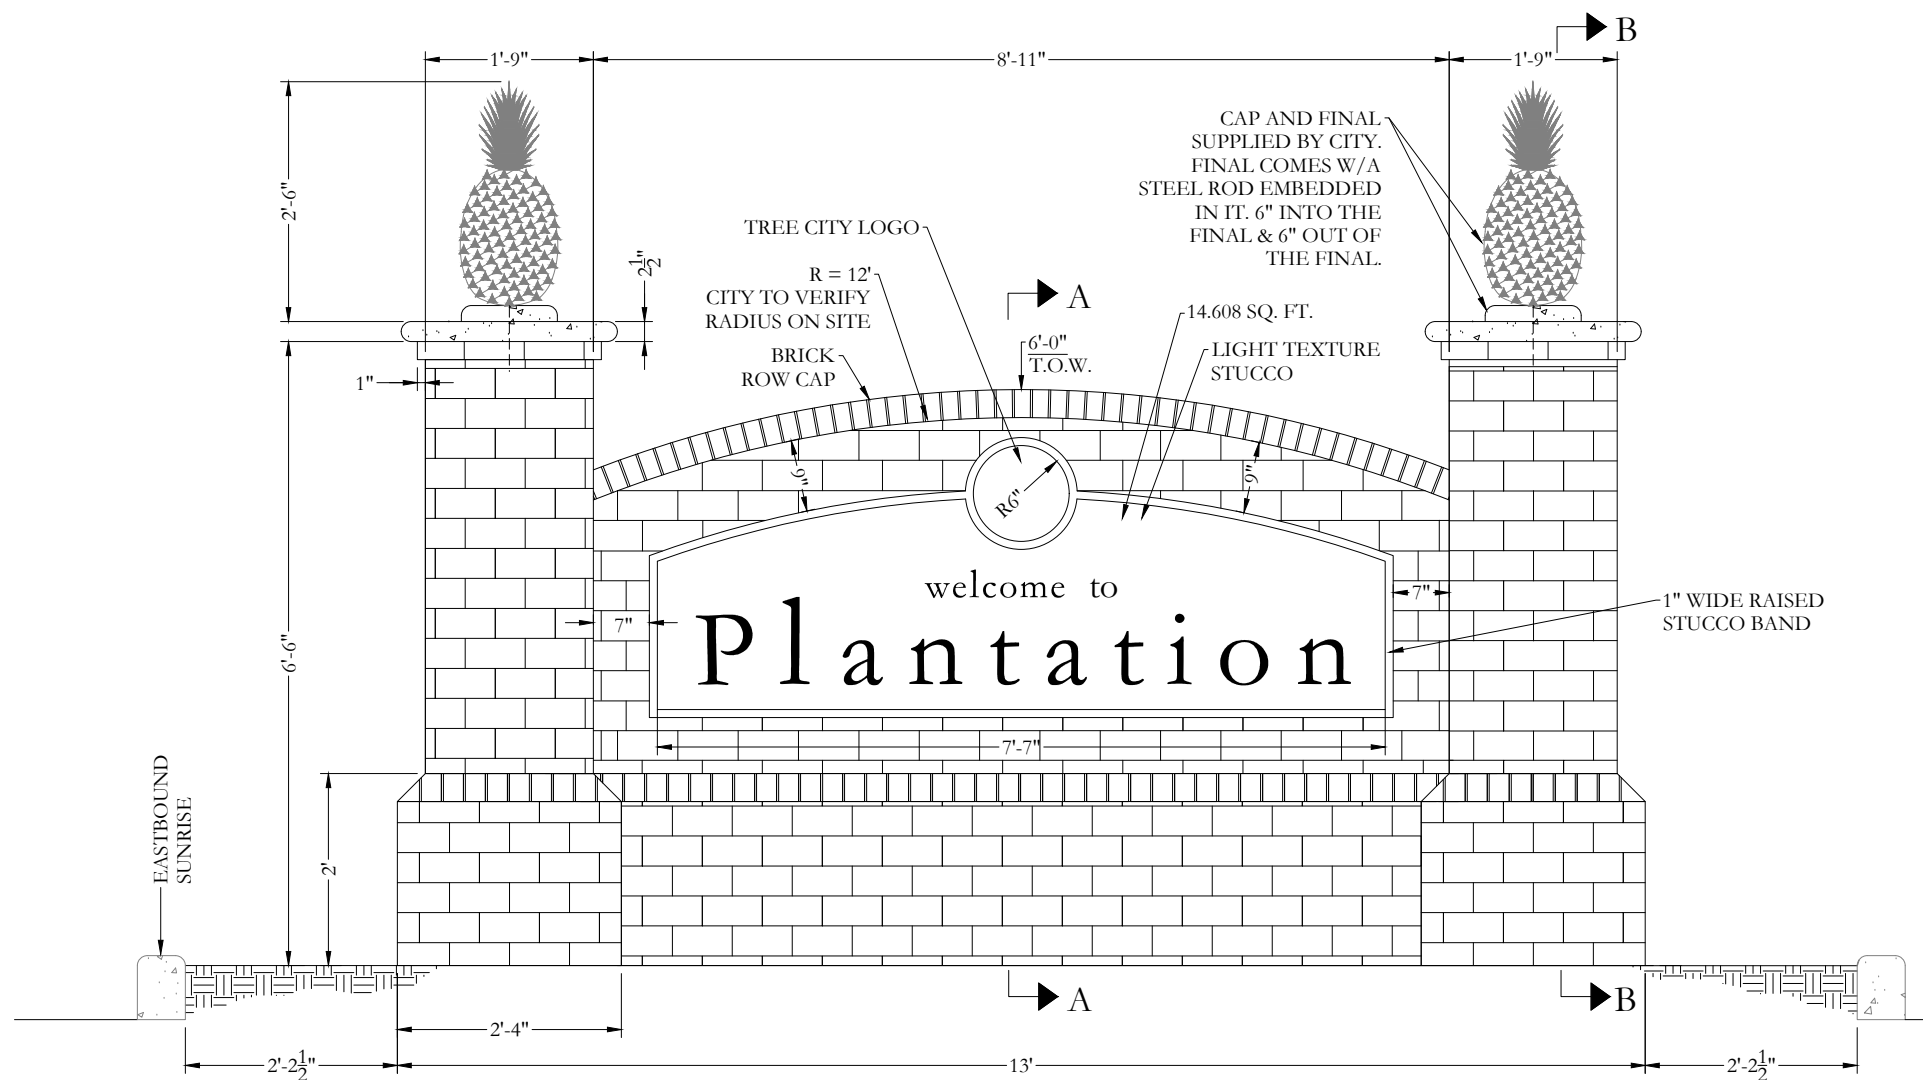

PROPOSED ENTRY SIGN ELEVATION



GENERAL CONSTRUCTION NOTES:

1.

WORK SHALL INCLUDE ALL ITEMS INDICATED ON THESE DRAWINGS UNLESS OTHERWISE NOTED.
2.

ALL APPLICABLE DEPOSITS AND FEES: DEPOSITS FOR UTILITIES INCLUDING WATER METER, TELEPHONE, AND ELECTRICAL SERVICE SHALL BE MADE BY THE GENERAL CONTRACTOR. PERMIT FEES, AS REQUIRED, SHALL BE PAID BY THE CONTRACTOR FOR THAT PORTION OF THE WORK.
3.

GENERAL CONTRACTOR SHALL REMOVE ALL CONSTRUCTION DEBRIS FROM THE JOB SITE. ANY PAINT SPECKS AND OTHER CONSTRUCTION MARKS SHALL BE REMOVED FROM ALL FINISHED SURFACES.
4.

ALL WORK SHALL BE PERFORMED IN ACCORDANCE WITH ALL CODES, RULES, REGULATIONS, AND RESTRICTIONS HAVING JURISDICTION. CONTRACTOR SHALL NOTIFY THE CITY IN WRITING PROMPTLY UPON OBSERVANCE OF ANY VARIATION BETWEEN THE CONTRACT DOCUMENTS AND ANY DIMENSIONS AND CONDITIONS ON THE JOB. ALSO NOTIFY THE CITY IN WRITING UPON OBSERVANCE OF ANY VARIATION BETWEEN THE CONTRACT DOCUMENTS AND ANY APPLICABLE CODES OR ORDINANCES OF REGULATORY AGENCIES.
5.

CONTRACTOR SHALL GUARANTEE ALL MATERIALS AND WORKMANSHIP FREE FROM DEFECTS FOR A PERIOD OF NOT LESS THAN ONE YEAR FROM DATE OF ACCEPTANCE. CORRECTION OF DEFECTS SHALL BE COMPLETED WITHOUT ADDITIONAL CHARGE AND AND WITHIN 15 DAYS OF NOTIFICATION.
6.

ALL CONSTRUCTION MATERIALS SHALL BE NEW AND SHALL BEAR UNDERWRITER'S LABELS WHERE APPLICABLE.
7.

SITE WORK : CLEAR ALL ORGANIC MATERIAL IF NECESSARY AND FILL WITH CLEAN SOIL.
8.

SOIL DENSITY TESTS SHALL BE TAKEN AND PAID FOR BY THE GENERAL CONTRACTOR.
9.


SLABS ON FILL : FILL AND BACKFILL TO BE COMPACTED TO 95% OF THE MAXIMUM DENSITY AT THE OPTIMUM MOISTURE AS DETERMINED BY STANDARD PROCTOR TEST OR BY SOIL ENGINEER'S RECOMMENDATIONS FOR OBTAINING REQUIRED BEARING CAPACITY. COMPACTION LAYERS NOT TO EXCEED 8 INCHES. SLABS ON FILL TO BE MINIMUM 4 INCHES THICK.
10.

ALL METAL BUILDING MATERIALS SHALL BE GALVANIZED OR CORROSION RESISTANT.

Topic #625-000-002
FDOT Design Manual

January 1, 2021

Table 212.11.1 Sight Distance for Left Turn from Highway

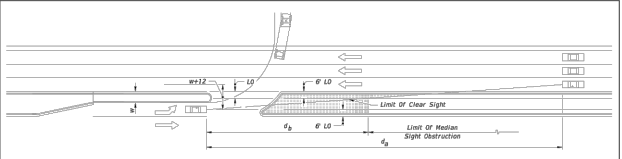

Design Speed (mph)	d _s (feet)								
	1 Lane Crossed			2 Lane Crossed			3 Lane Crossed		
	P	SU	Comb.	P	SU	Comb.	P	SU	Comb.
25-30	245	290	330	265	320	365	290	350	395
35	285	335	385	310	370	425	335	410	460
40	325	385	440	355	425	485	385	465	525
45	365	430	495	400	475	545	430	525	590

- Notes:
- (1)

Provide a lateral offset (LO) of 6' as shown in the diagram above. d_s may be determined by the equation d_s = d_s (w/(w+12)). For roadways with non-restricted conditions, d_s and d_s should be based on the geometry for the left turn storage and on clear zone widths.
- (2)

For wide medians where the turning vehicle can approach the through lane at or near 90°, use d values from tables in *Exhibits 212-6* and *212-7*. (The clear sight line origin is assumed to be 14.5 feet from the edge of the near travel lane.

212.11.5 On-Street Parking

Table 212.11.2 provides parking restrictions for intersections; including mid-block crossings and roundabout approaches. For additional information, see the following:

- **FDM 210.2.3** for additional information concerning on-street parking.
- **FDM 222.2.6** for information concerning curb extensions (bulb-outs).
- **Chapter 316, [Florida Statutes \(F.S.\)](#)**, for laws governing parking spaces.

212-Intersections

25

Topic # 625-000-015
Manual of Uniform Minimum Standards
for Design, Construction and Maintenance
for Streets and Highways

2018

Table 4 – 2 Lateral Offset (feet)

Roadside Feature	Urban Curbed Roadways Design Speed ≤ 45 (mph)	All Other
Above Ground Objects ¹	4 ft. from Face of Curb ²	Clear Zone Width
Drop Off Hazards ³	Clear Zone Width	Clear Zone Width
Water Bodies	Clear Zone Width	Clear Zone Width
Canal Hazards	See Section B.2.c	See Section B.2.c

1. Above ground objects are anything greater than 4 inches in height and are firm and unyielding or do not meet crashworthy or breakaway criteria. For urban curbed areas ≤ 45 mph this also includes crashworthy or breakaway objects except those necessary for the safe operation of the roadway.

2. May be reduced to 1.5 ft. from Face of Curb on roads functionally classified as Local Streets and on all roads where the 4 ft. minimum offset cannot be reasonably obtained and other alternatives are deemed impractical.

3. Drop off hazards are:
- a.

Any vertical faced structure with a drop off (e.g. retaining wall, wing-wall, etc.) located within the Clear Zone.
- b.

Slopes steeper than 1:3 located within the Clear Zone.
- c.

Drop-offs with significant crash history.

B.2 Drainage Features

Drainage design is an important aspect of the long-term performance of a roadway, and to achieve an effective design, drainage features are necessary in close proximity to travel lanes. These features include ditches, curbs, and drainage structures (e.g. transverse/parallel pipes, culverts, endwalls, wingwalls, and inlets). The placement of these features is to be evaluated as part of roadside safety design. Refer to **Chapter 20 – Drainage** for information regarding proper hydraulic design.

Roadside Design

4-12



Plantation
the grass is greener

CITY OF PLANTATION
ENGINEERING DEPT.

401 NW 70TH TERRACE, PLANTATION, FL 33317
TEL. (954) 797-2282 FAX (954) 797-2761

SAMIRASHALAN P.E.
CITY ENGINEER

DATE

REVISIONS

COMMENT

BY

DATE

No.

PROJECT
Welcome to Plantation Entry Sign

DRAWING
General Notes and Standard Details

SCALE
N.T.S.

DESIGNED

DATE

DRAWN BY

DATE

CHECKED BY

DATE

DRAWING NO.

C-03

PROJECT NO.

CP22-06

SHEET NO.


4 of 6

REVISIONS		COMMENT
No.	DATE	BY

Saad El-Hage, PE
"Structural Consultant"
Saad El-Hage
Consulting Engineers, Inc.
5601 NW 9th Ave, Suite 206
Fort Lauderdale, FL 33309


PROJECT: **Welcome to Plantation Entry Sign**
DRAWING: **Sections and Structural Notes**

SCALE: As Shown	
DESIGNED	DATE
DRAWN BY L. Raño	DATE 9/29/2022
CHECKED BY J.P.	DATE 9/29/2022
DRAWING NO. S-01	
PROJECT NO. CP22-06	
SHEET NO. 5 of 6	

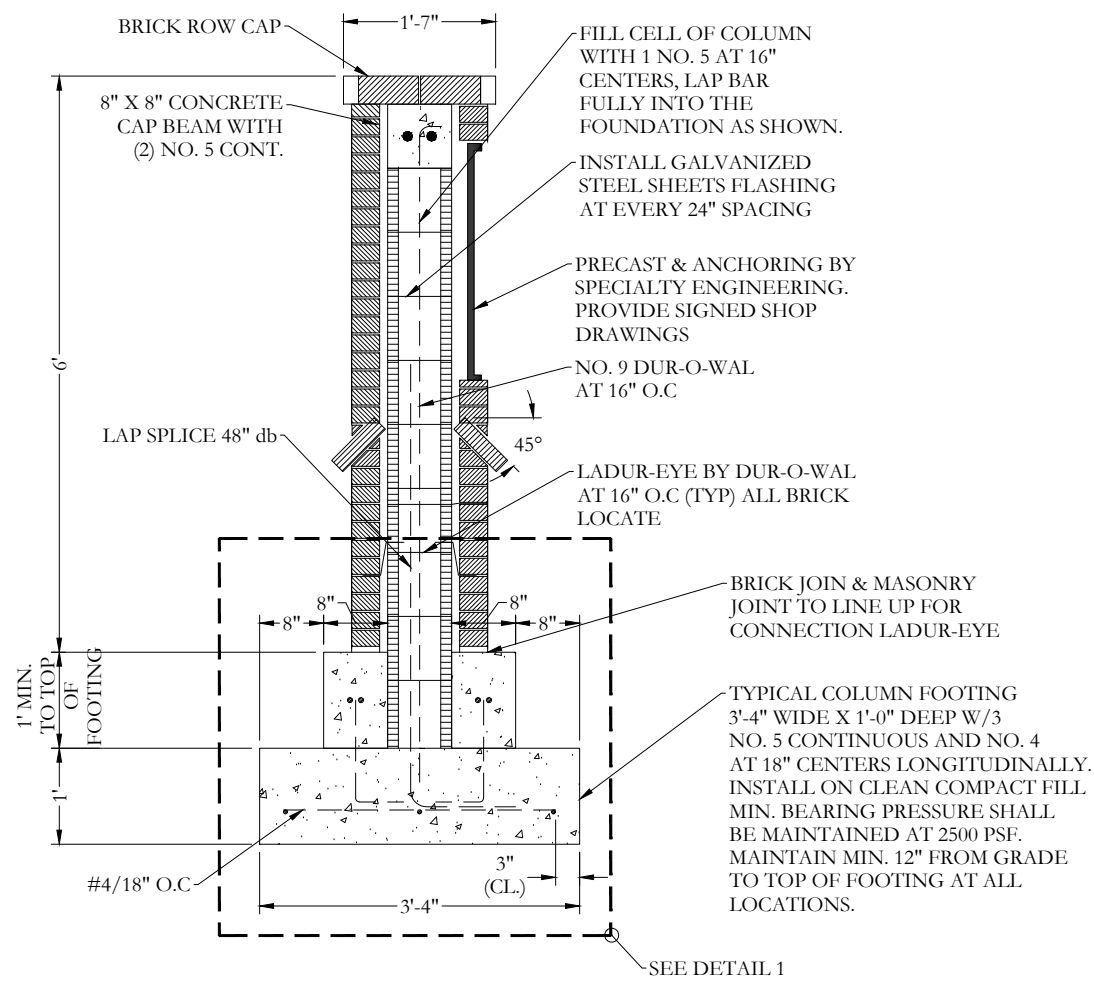

SECTION A-A

FINAL FINISHES, COLOR SELECTIONS, PRE-CAST CONCRETE ITEM SELECTIONS, BRICK SELECTION, AND SIGNAGE SHALL BE BY THE CITY.

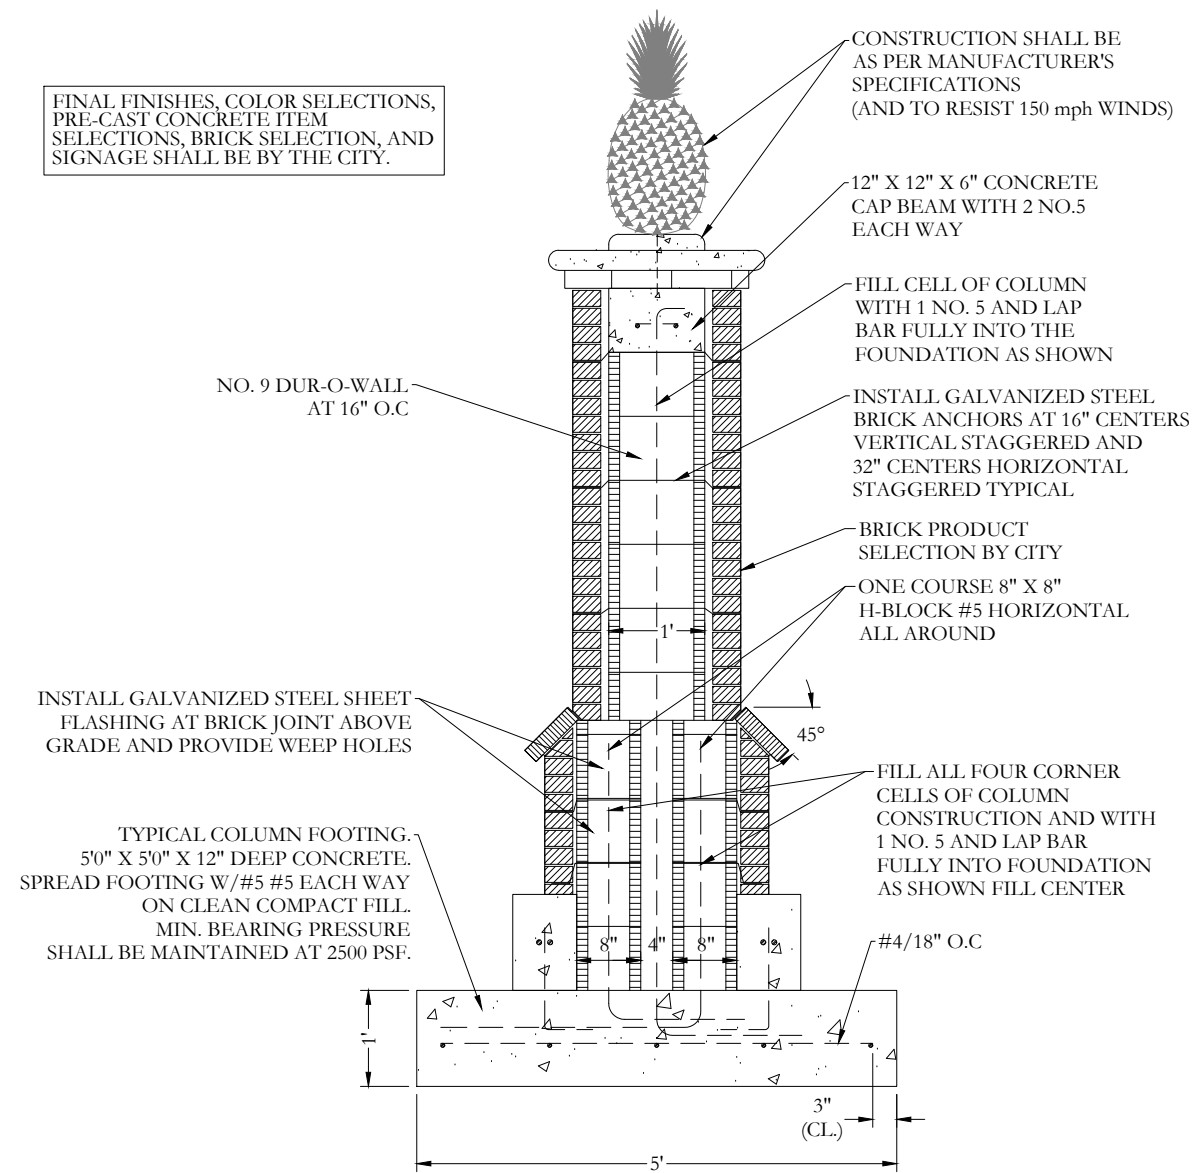

SECTION B-B

STRUCTURAL NOTES:

1.

CONCRETE GENERAL : UNLESS OTERWISE CALLED FOR IN SPECIFICATIONS OR DRAWINGS, ALL CONCRETE WORK SHALL CONFORM TO ALL REQUIREMENTS AND RECOMMENDATIONS OF ACI-301-72 'SPECIFICATION FOR STRUCTURAL CONCRETE FOR BUILDINGS'.
2.

CONCRETE TO BE A MIX DESIGNED IN ACCORDANCE WITH ASTM C-84-72 TO ACHIEVE A STRENGTH AS STATED BELOW, AT 28 DAYS, WITH A PLASTIC AND WORKABLE MIX. A CERTIFICATE OF MANUFACTURER'S MIX AND STRENGTH IS TO BE PROVIDED. NO WATER TO BE ADDED AFTER THE TRUCK LEAVES THE PLANT WITHOUT APPROVAL OF ENGINEER OR PLANT ENGINEER. PLANT CONTROL IS REQUIRED. MAXIMUM MIX TIME AT POINT OF DEPOSIT IS 90 MINUTES. FC = 3000 PSI.
3.

REINFORCING STEEL BARS TO BE A165-GRADE 60 UNLESS OTHERWISE NOTED, FREE FROM OIL, LOOSE SCALE, AND LOOSE RUST, AND BENT, LAPPED, PLACED, SUPPORTED, AND FASTENED ACCORDING TO THE MANUAL OF STANDARD PRACTICE FOR DETAILING CONCRETE STRUCTURES ACI-318-65 AND THE BUILD CODE REQUIREMENTS FOR REINFORCED CONCRETE ACI-318-77. IN CASSE OF CONFLICT, ACI-318-71 SHALL TAKE PRECEDENCE.
4.

ALL FOOTINGS DESIGNED FOR 2500 PSFSOIL BEARING. CONTRACTOR TO NOTIFY ENGINEER IN WRITING IF SOIL CONDITIONS ARE FOUND TO BE UNSUITABLE TO OBTAIN DESIRED BEARING CAPACITY.
5.

TYPICAL 'FILLED CELL' MASONRY CONSTRUCTION SHALL CONSIST OF GROUT OR CONCRETE FILLED 'FULL HEIGHT' MASONRY CELL WITH 1 #5 VERTICAL CONTINUOUS AND 1 #5 'J BAR' ANCHORED INTO FOOTING AND LAPPED 2'-6" MINIMUM.

a)


HOLLOW MASONRY UNITS SHALL CONFORM TO ASTM C-90, TYPE II, GRADE N, SQUARE END WITH A MINIMUM AVERAGE CONCRETE STRENGTH OF $f_m = 1500$ psi.

b)

MORTAR SHALL CONFORM TO ASTM C-270, TYPE M WITH A 28-DAY STRENGTH OF 2,500 psi.

c)

FILL CELLS GROUT SHALL HAVE A MINIMUM STRENGTH OF 3,000 psi WITH HIGH WATER TO CEMENT RATIO MINIMUM OF 10" SLUMP. GROUT SHALL CONFORM TO ASTM C-476 AND FBC 2122-8.

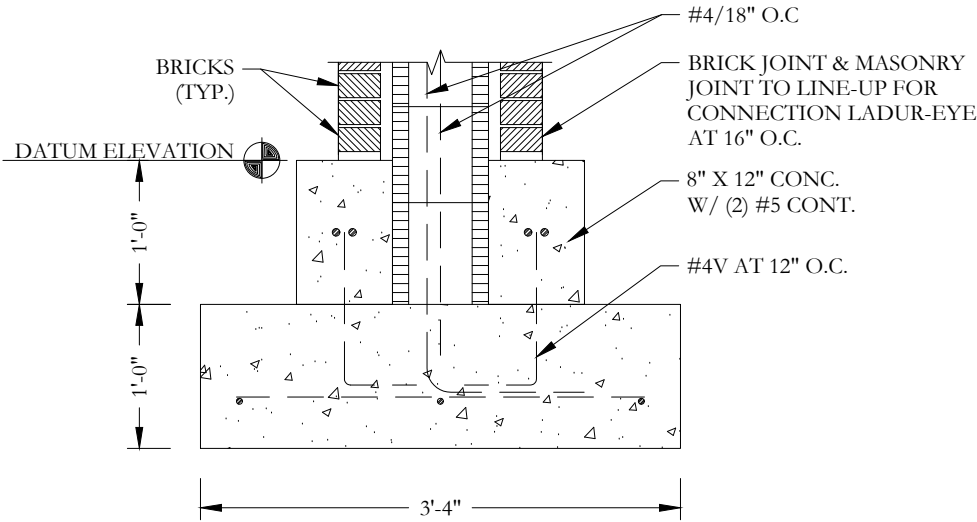

DETAIL 1

REVISIONS		COMMENT	
No.	DATE	BY	

Saad El-Hage, PE
"Structural Consultant"
Saad El-Hage
Consulting Engineers, Inc
5601 NW 9th Ave. Suite 206
Fort Lauderdale, FL 33309

PROJECT	Welcome to Plantation Entry Sign
DRAWING	Details and Structural Notes

SCALE	
As Shown	

DESIGNED	DATE
DRAWN BY L. Riano	DATE 9/29/2022
CHECKED BY J.P.	DATE 9/29/2022

DRAWING NO.
S-02
PROJECT NO.
CP22-06
SHEET NO.